UNIVERSITÀ DI PISA

Giovanna Rocha Santos Mangabeira Araujo

BUILDING ENGINEERING AND
ARCHITECTURE STUDENT
2016 -2026

PORTFOLIO

4 of my favorite projects

Floor Plan with profection of beams
1:200

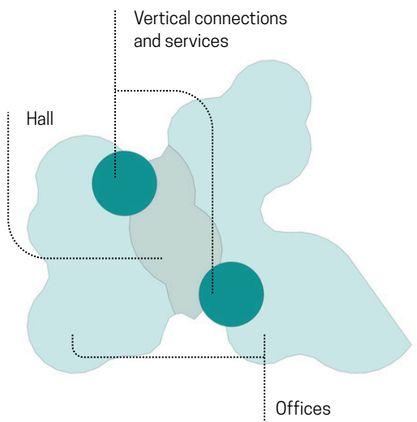

Visualization of the layout of the building's functions

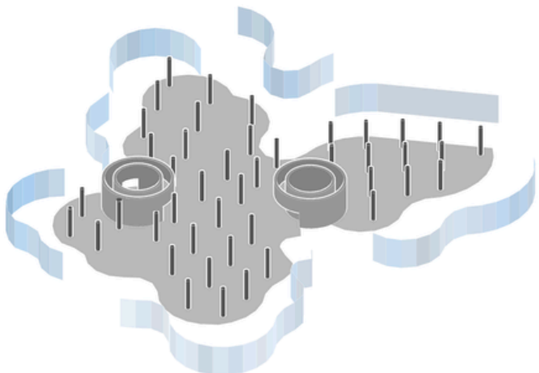

Exploded view of one of the floors
The supporting structure, represented only in a few sketches, is a steel skeleton, and the curvilinear cantilevered floors are covered with a uniform skin of transparent glass.

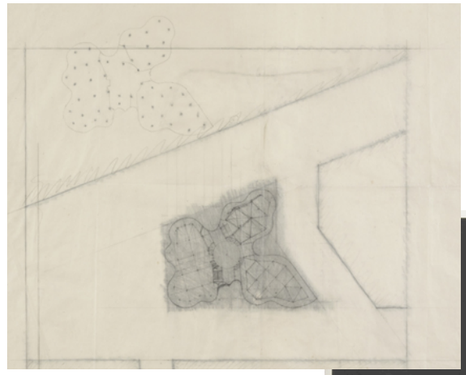

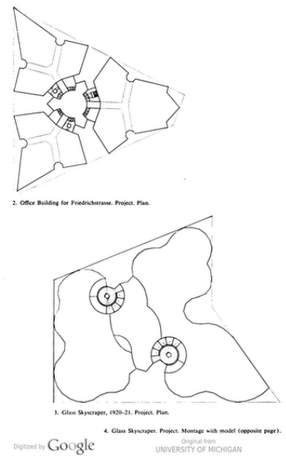

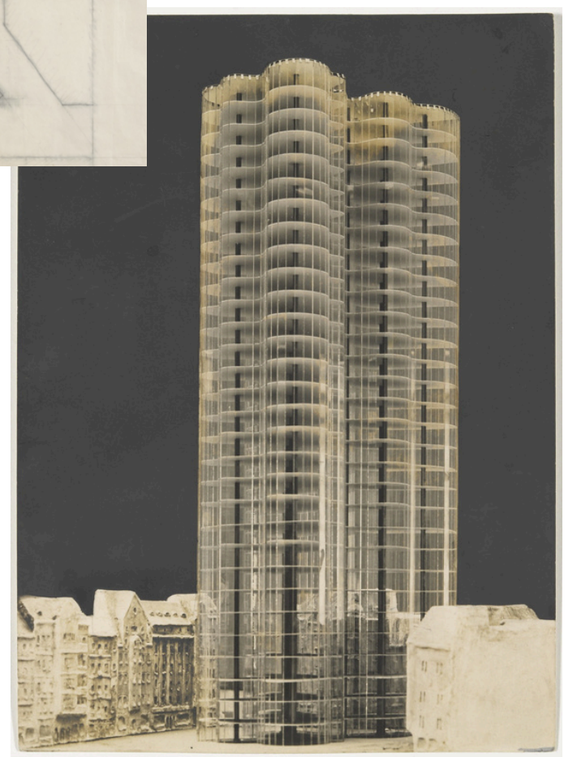

Architect
Ludwig Mies van der Rohe
Designed in
1922
Location
Berlin, Germany

Sources from G, No.1

Mies Van der Rohe in Berlin
The Glass Skyscraper

1 Developed for an academic workshop, the project consists of an analytical study and 2D/3D CAD modeling of plans and elevations, together with photomontage of the glass skyscraper designed by Ludwig Mies van der Rohe.

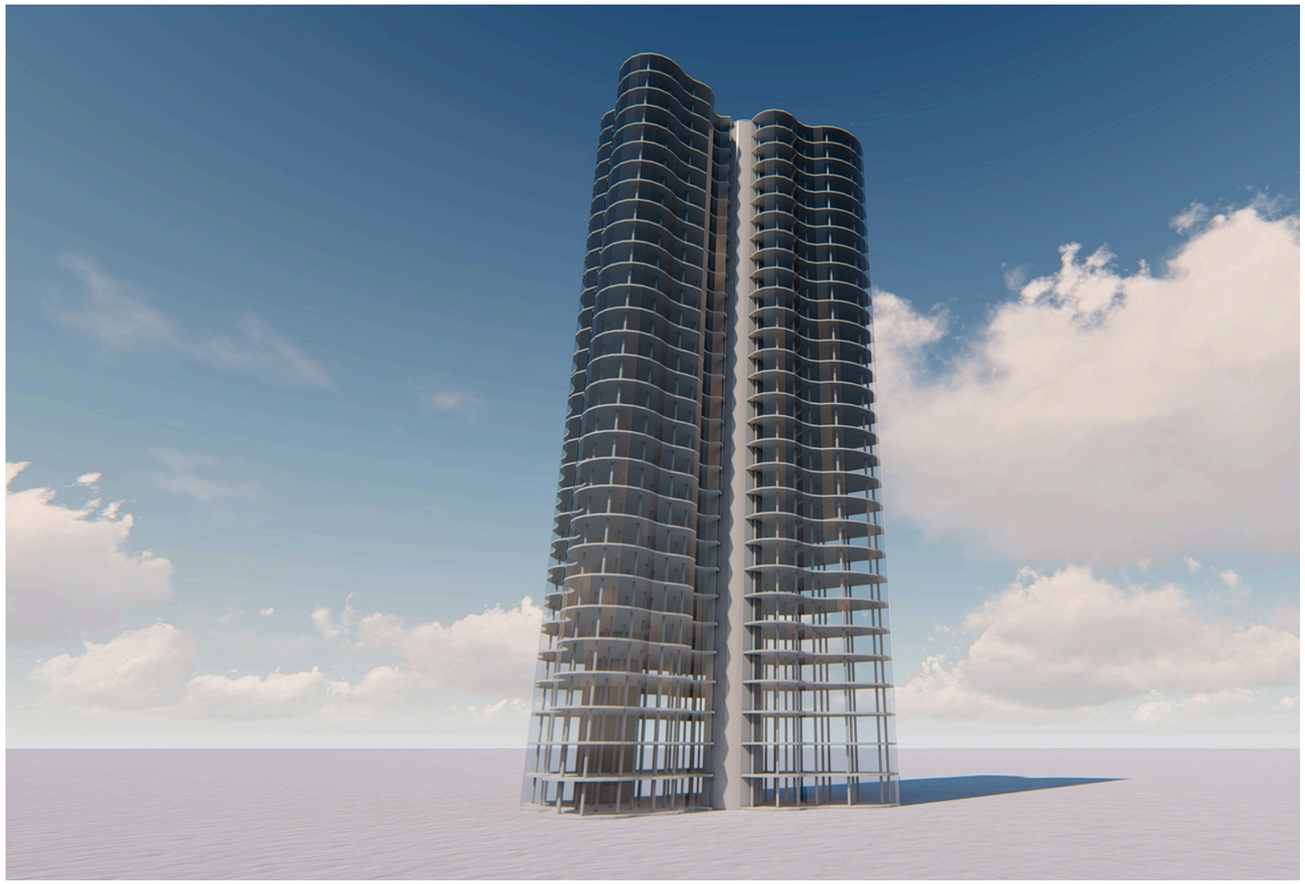

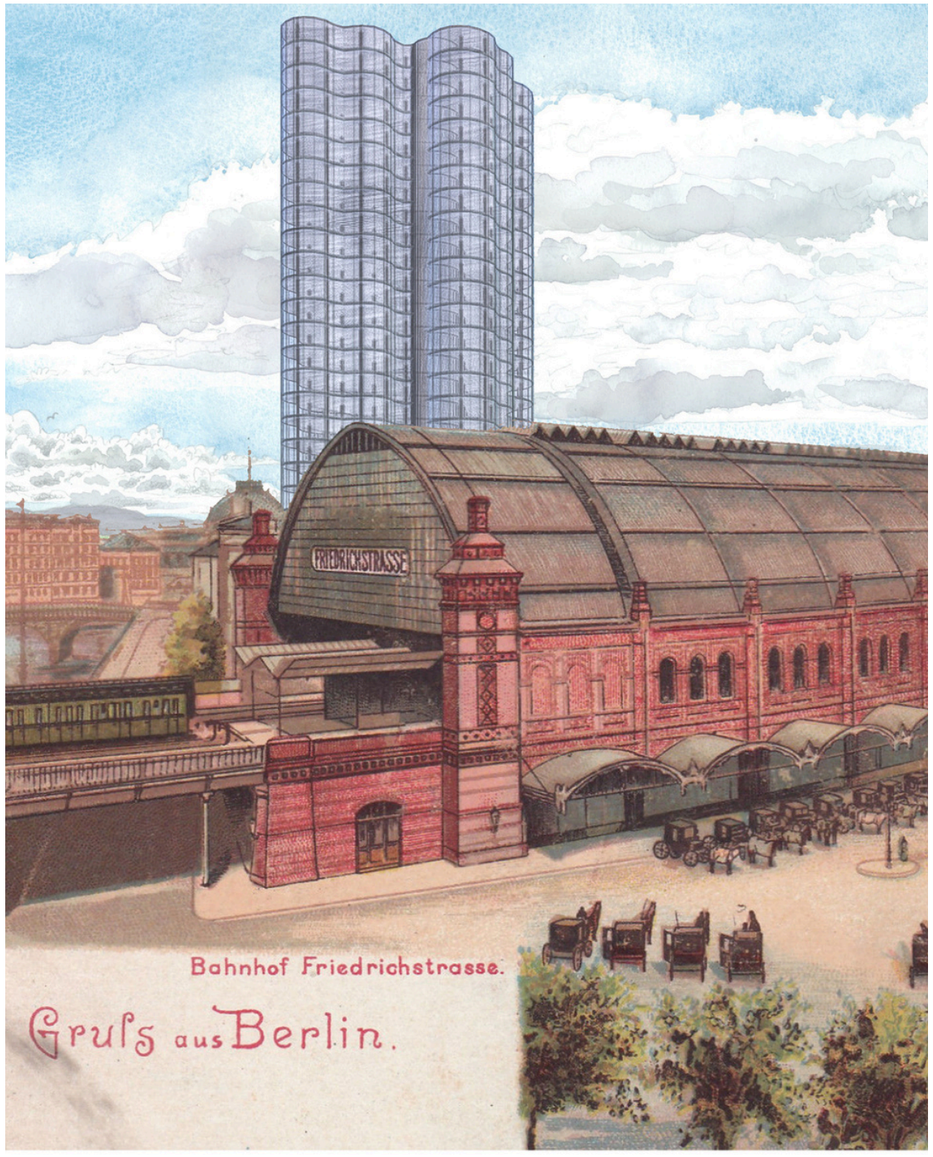

Renders

Tools:
Rhino
Lumion
Photoshop

ESPLOSO ASSONOMETRICO

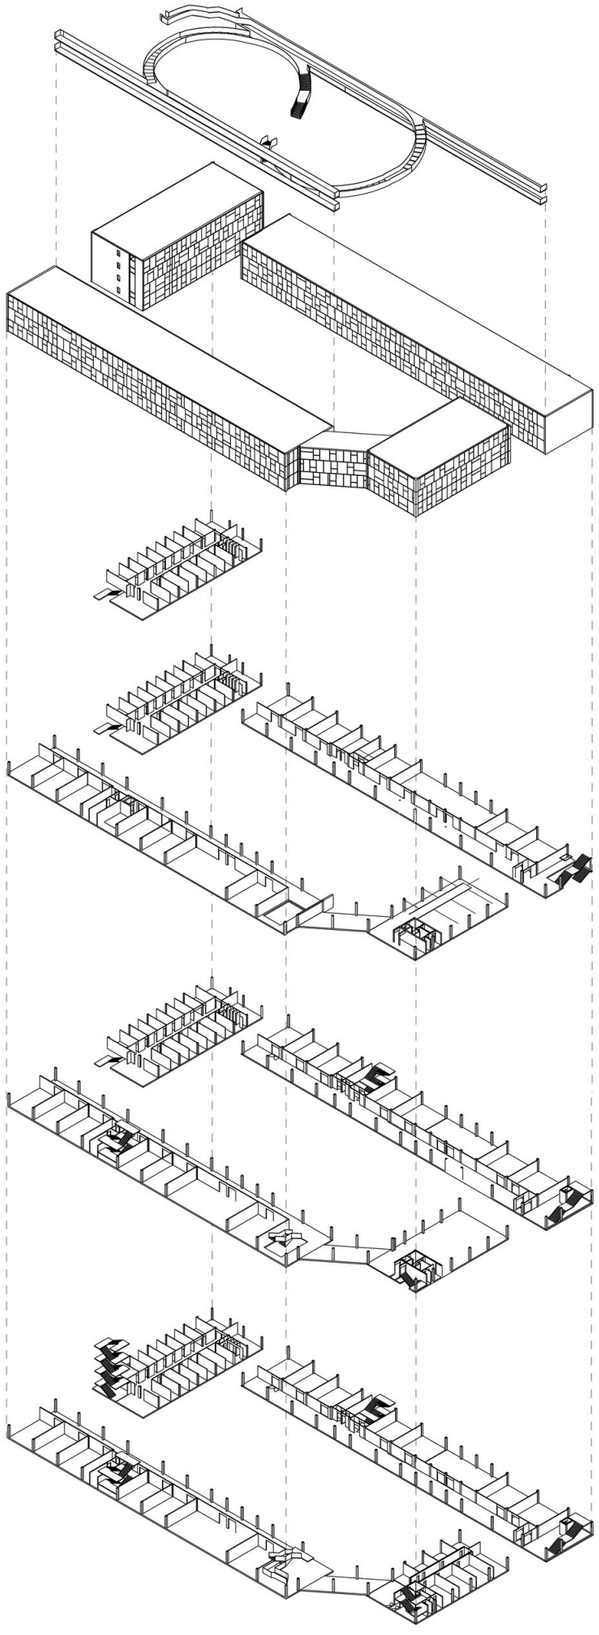

RAMPA

INVOLUCRO

TERZO PIANO

SECONDO PIANO

PRIMO PIANO

PIANO TERRA

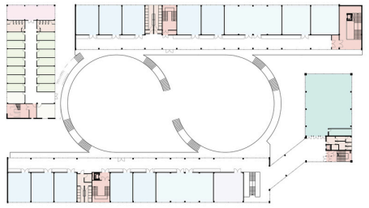

PIANTA SECONDO PIANO

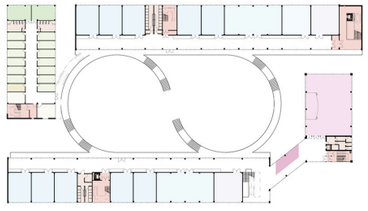

PIANTA PRIMO PIANO

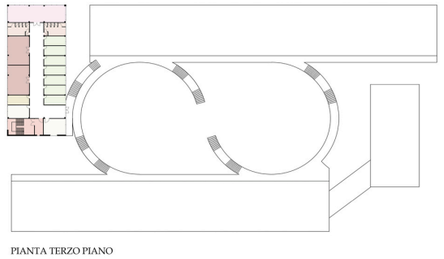

PIANTA TERZO PIANO

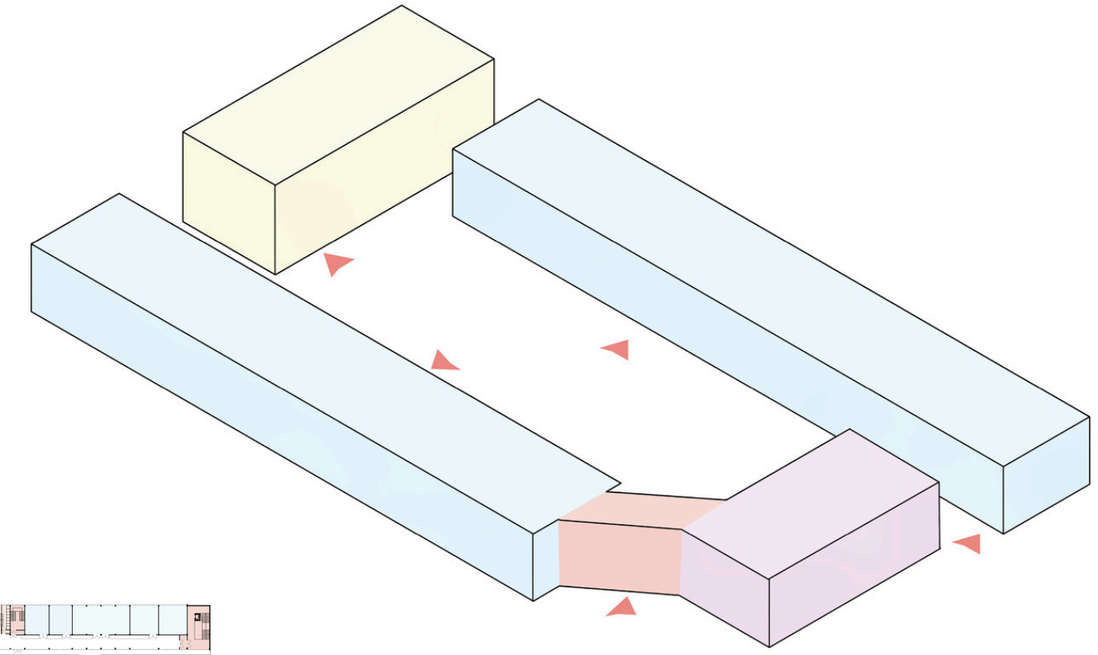

UFFICI

AULE

ATRIO

SEGRETERIA, AULA MAGNA, BIBLIOTECA

INGRESSI

2

Project of a new department of Architecture building for the University of Pisa

The aim of the project was to design a building complex that accomodates university life,In compliance with current regulations on the size of spaces inside public buildings, the volumes are conceived as simple parallelepipeds, sized and arranged according to their different functions. The layout is organized around a central courtyard, with the aim of maximizing the area dedicated to green spaces.

RENDERS

MASTERPLAN

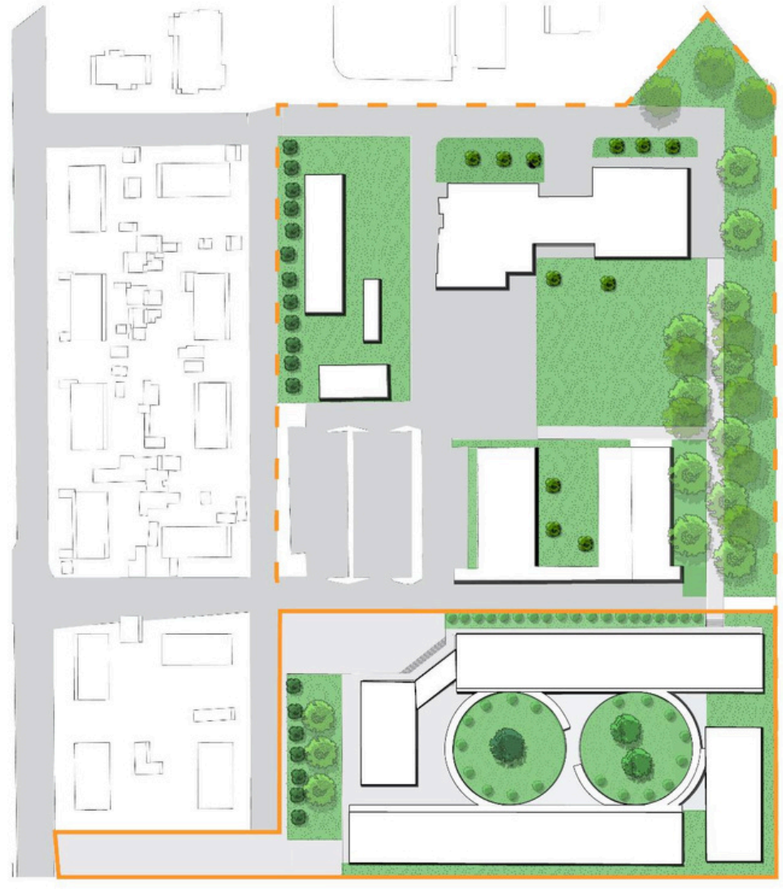

The central ramp allows students and academic staff to move from each building towards each of its parts.
The white ramps are inspired by Luberkin's project for the London zoo.
The ramps characterize the entire project, and are not a simple path of connection, but the strength of the structure.

UNIVERSITÀ DI PISA | CdLM in Ingegneria Edile-Architettura | a.a. 2020-2021

CORSO DI RESTAURO E CONSOLIDAMENTO

PROGETTO DI RESTAURO DELLA CERTOSA DI CALCI

Docenti: Ing. S. Landi (resp.), Ing. S. Caprili (resp.), Prof. Arch. P. Ruschi, Arch. G. Bacci. Assistente: Arch. G. Puccini.

Studenti: Marco Orlandi, Giovanna Rocha Santos

RILIEVO GEOMETRICO

Data: 08 aprile 2024

Scala: 1:50

Numero tavola: G 08

Tipo di elaborato: SEZIONI

Sezione AA

0 1 2 5M

scala 1:50

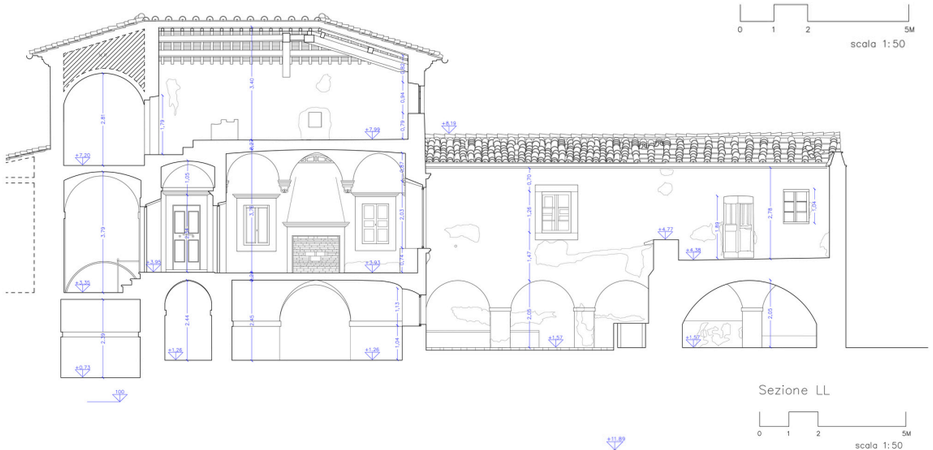

Sezione LL

0 1 2 5M

scala 1:50

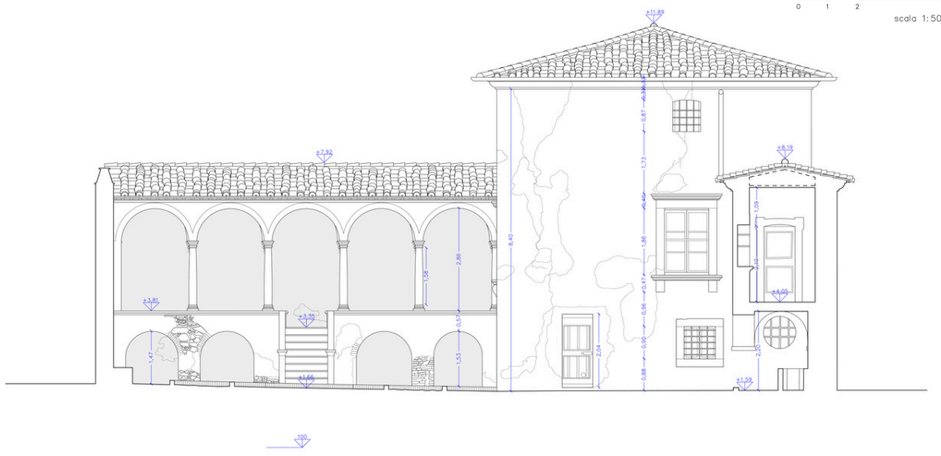

Sezione CC

0 1 2 5M

scala 1:50

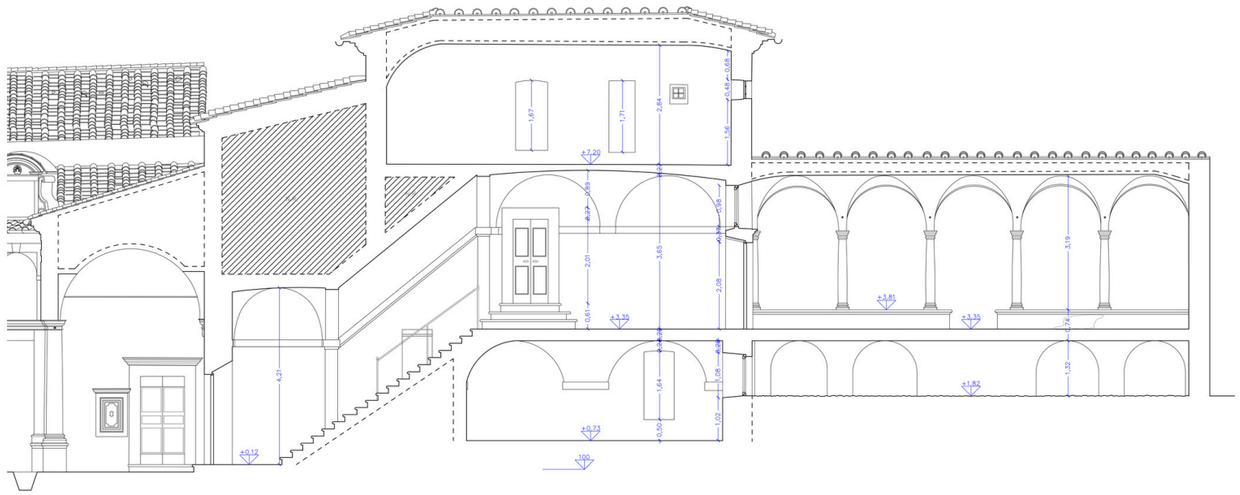

Sezione DD

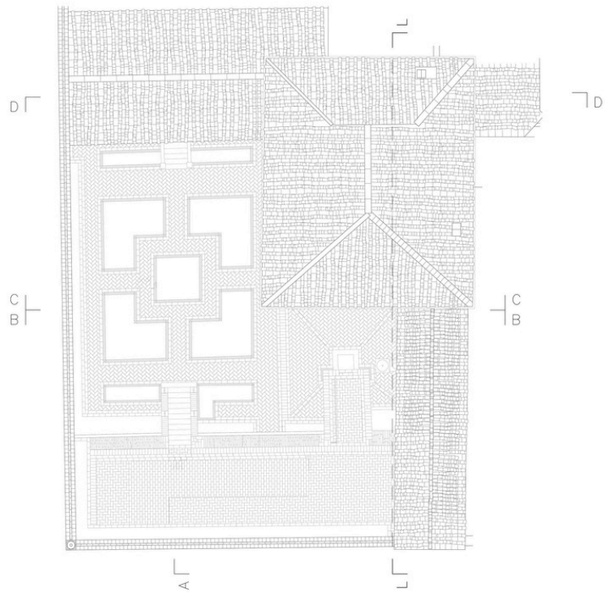

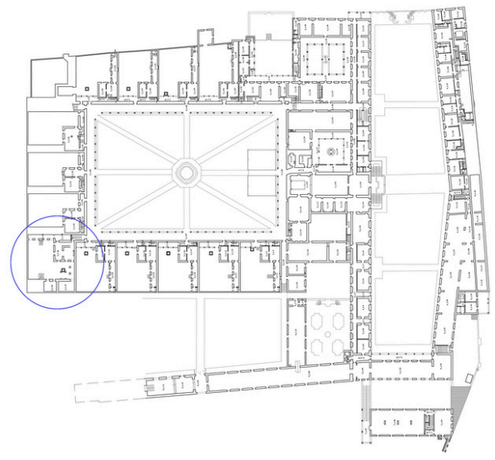

Restoration and Strengthening Design of the Certosa di Calci Monastery

SURVEYING FLOOR-PLANS, SECTIONS AND ELEVATIONS

4

During the laboratory activities, in addition to graphic surveying and analysis of materials and deterioration, documentary research and specific checks on the architectural text, which were also carried out through various seminars. This in this workshop I also got to gain experience on restoration techniques for both masonry and surfaces (plaster, wall paintings, coatings, etc.).

Sezione LL

0 1 2 5M

scala 1:50

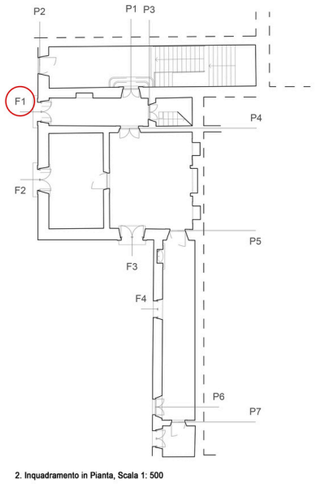

2. Inquadramento in Pianta, Scala 1: 500

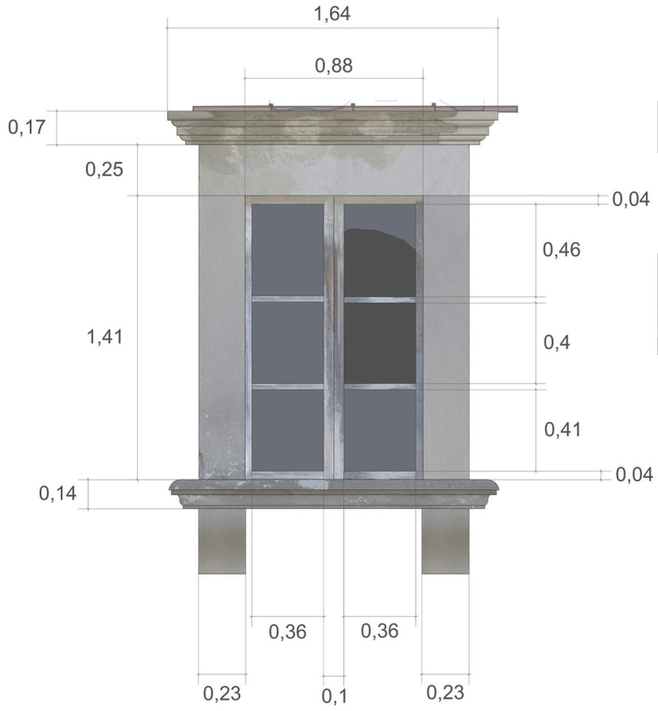

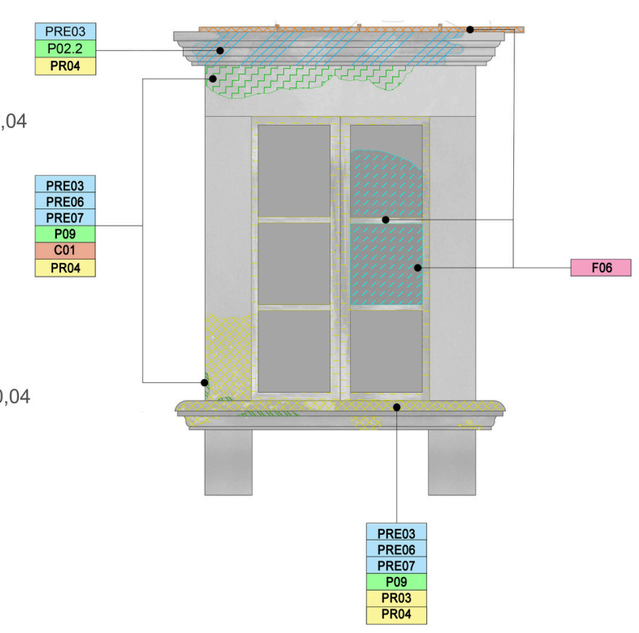

Restoration and Strengthening Design of the Certosa di Calci Monastery

CURRENT STATE

Thank You

This portfolio represents part ofmy journey as a student of Building Engineering and Architecture: a journey guided by curiosity, responsibility and attention to issues of sustainability and the social impact of architectural design. I believe in architecture as a concrete tool for improving the quality of cities, spaces and the relationships of its users, through simple, conscious and well-constructed solutions. I am motivated to join a firm where I can learn on the job, contribute seriously and grow within a collaborative design process. I bring with me method, adaptability and a strong willingness to get involved: qualities that I have developed both in my studies and in my work and community service experiences. I would be happy to discuss my work in person and explore how I can make a concrete contribution to your projects.